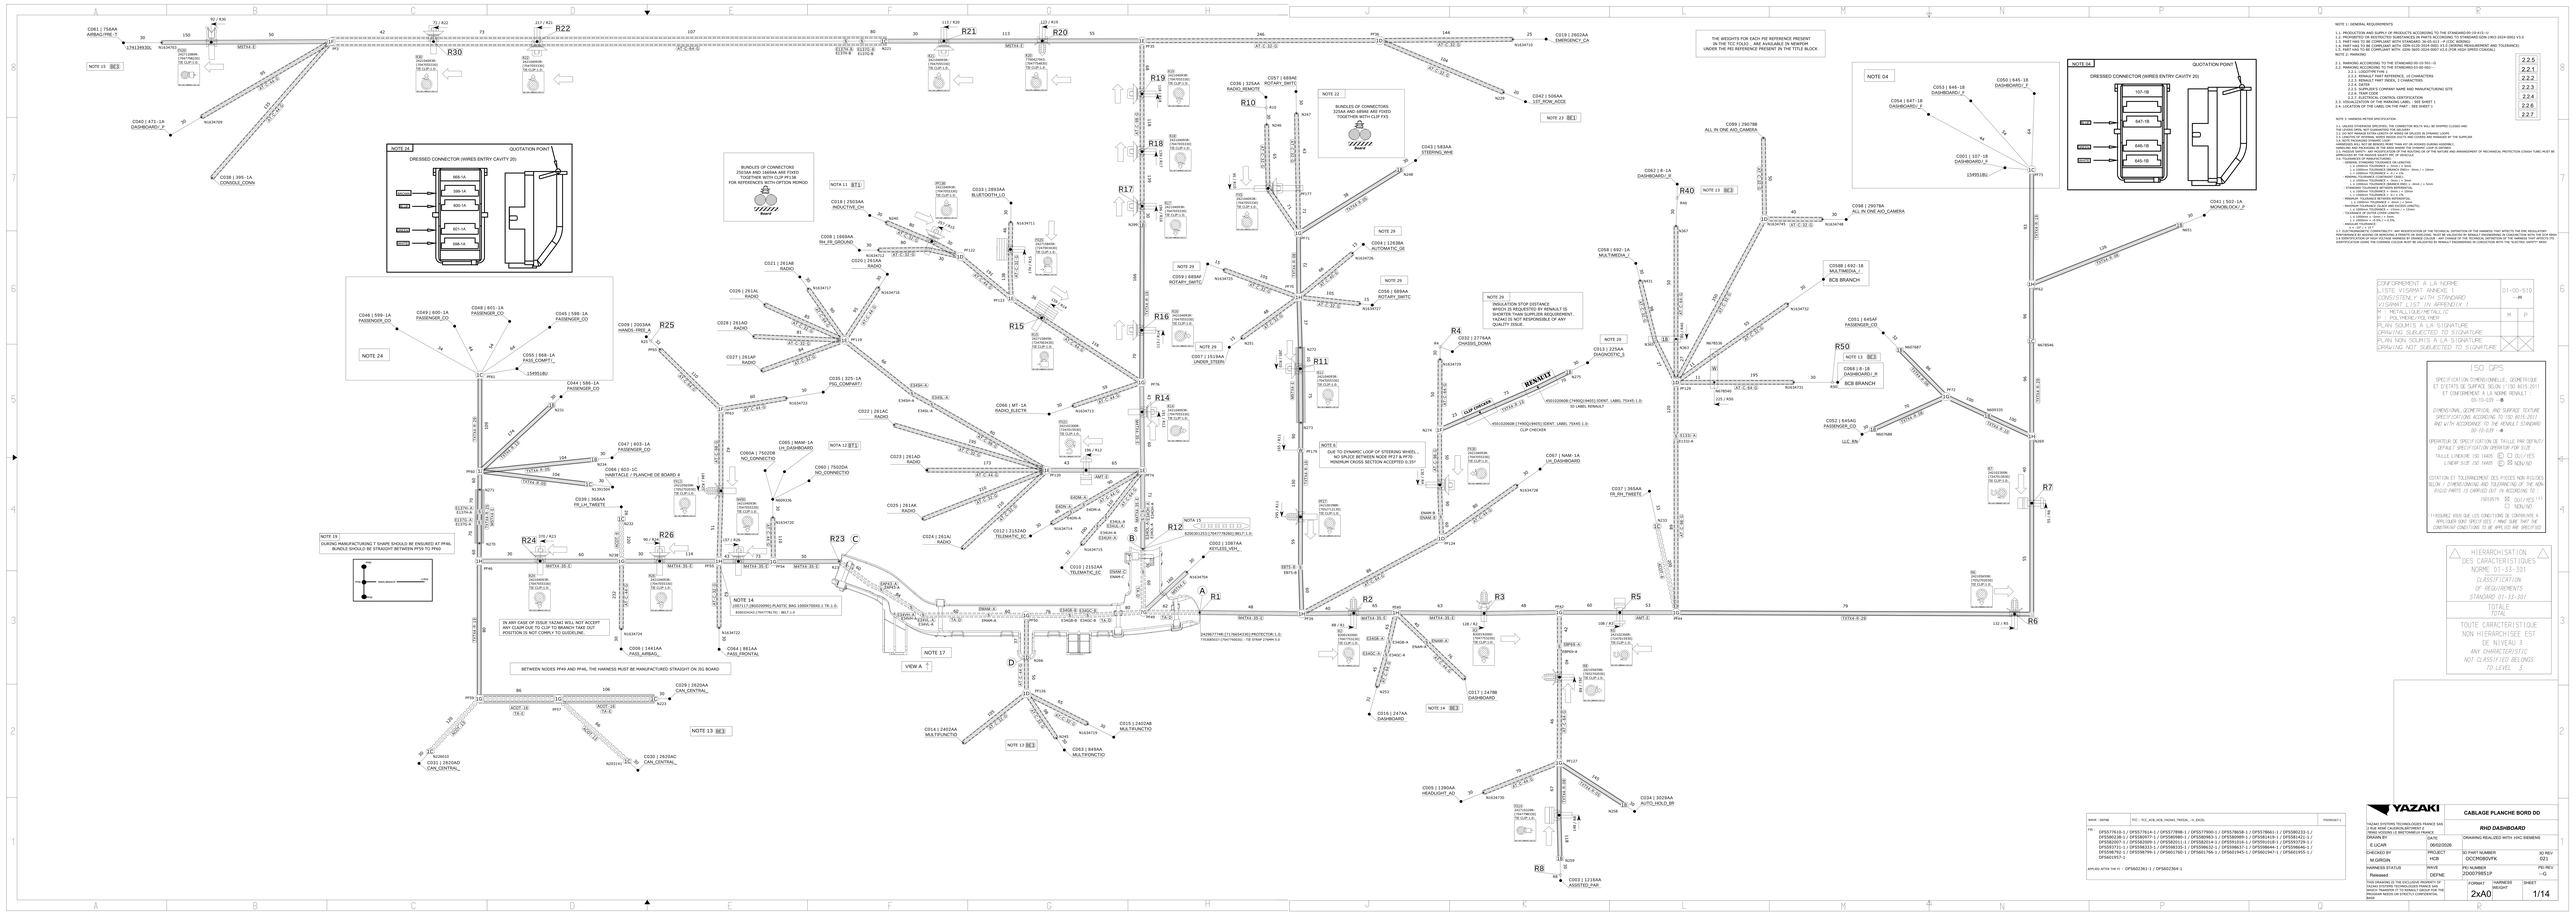

C061 | 756AA
AIRBAG-TYPE 7
NOTE 15
C040 | 471- 1A
DASHBOARD_F
C038 | 395- 1A
CONSOLE_CONN
NOTE 24
DRESSED CONNECTOR (WIRES ENTRY CAVITY 20)
QUATATION POINT
668-1A
599-1A
600-1A
601-1A
598-1A
C046 | 599- 1A
PASSENGER_CO
C049 | 600- 1A
PASSENGER_CO
C048 | 601- 1A
PASSENGER_CO
C045 | 598- 1A
PASSENGER_CO
C055 | 668-1A
PASS_COMPT |
C044 | 596- 1A
PASSENGER_CO
C047 | 603- 1A
PASSENGER_CO
C066 | 603- 1C
HABITACLE / PLANCHE DE BOARD 4
C060A | 750208
NO_CONNECTO
C065 | MAM- 1A
LH_DASHBOARD
C061 | 750208
NO_CONNECTO
C039 | 366AA
FR_LH_TWEETE
C064 | 861AA
PASS_FRONTAL
C006 | 1441AA
PASS_AIRBAG_
C029 | 2620AA
CAN_CENTRAL
C030 | 2620AC
CAN_CENTRAL
C031 | 2620AD
CAN_CENTRAL
NOTE 19
DURING MANUFACTURING T SHAPE SHOULD BE ENSURED AT PP46, BUNDLE SHOULD BE STRAIGHT BETWEEN PP39 TO PP60
PP39
PP46
PP60
BUNDLE
TAPE
BUNDLES OF CONNECTORS 2520AA AND 1669AA ARE FIXED TOGETHER WITH CLIP PF13B FOR REFERENCES WITH OPTITON MOMOD
NOTA 11
C016 | 2503AA
INDUCTIVE_CH
C008 | 1668AA
RH_FR_GROUND
C021 | 261AB
RADIO
C026 | 261AL
RADIO
C028 | 261AO
RADIO
C027 | 261AP
RADIO
C035 | 325-1A
PSG_COMPARTI
C033 | 2893AA
BLUETOOTH_LO
C023 | 261AD
RADIO
C022 | 261AC
RADIO
C025 | 261AK
RADIO
C024 | 261AJ
RADIO
C012 | 2152AD
TELEMATIC_EC
C010 | 1532AA
TELEMATIC_EC
C002 | 1587AA
KEYLESS_VEH
NOTA 12
NOTA 15
NOTE 14
20577-27-2B0200MG PLASTIC BAG 1500X700MG 3 TR L D
R2000304G1704777B1-MG-1-0
C009 | 2003AA
HANDS-FREE_A
C007 | 1519AA
UNDER_SYSEM
C004 | 1283A
AUTOMATIC_DE
C056 | 689AA
ROTARY_SWITC
C057 | 689AE
ROTARY_SWITC
C036 | 325AA
RADIO_REMOTE
C043 | 583AA
STEERING_WHE
C042 | 506AA
1ST_ROW_ACCE
C019 | 2602AA
EMERGENCY_CA
NOTE 22
BUNDLES OF CONNECTORS 5726A AND 5869C ARE FIXED TOGETHER WITH CLIP FX5
NOTE 23
NOTE 29
INSULATION STOP DISTANCE WHICH IS REQUESTED BY RENAULT TO ENSURE THE SAFETY OF THE EQUIPMENT. YAZAKI IS NOT RESPONSIBLE OF ANY QUALITY ISSUE.
NOTE 6
DUE TO DYNAMIC LOOP OF STEERING WHEEL : NO SPLICE BETWEEN NODE PF27 & PF70 MINIMUM CROSS SECTION ACCEPTED 0.35²
C099 | 2907BB
ALL IN ONE AIO_CAMERA
C062 | 8-1A
DASHBOARD_F
C098 | 2907BA
ALL IN ONE AIO_CAMERA
C041 | 502-1A
MONOBLOCK_F
C058 | 692-1A
MULTIMEDIA_I
C088 | 692-1B
MULTIMEDIA_I
C013 | 2254A
DIAGNOSTIC_3
C087 | NAM-1A
LH_DASHBOARD
C037 | 365AA
FR_RH_TWEETE
C051 | 645AF
PASSENGER_CO
C068 | 8-1B
DASHBOARD_F
C052 | 645AG
PASSENGER_CO
C053 | 646-1B
DASHBOARD_F
C050 | 645-1B
DASHBOARD_F
C054 | 647-1B
DASHBOARD_F
C001 | 197-1B
DASHBOARD_F
134951BU
NOTE 04
NOTE 16
DRESSED CONNECTOR (WIRES ENTRY CAVITY 20)
QUATATION POINT
107-1B
647-1B
646-1B
645-1B
C117 | 2478B
DASHBOARD
C116 | 2474A
DASHBOARD
C015 | 2402AB
MULTIFUNCTIO
C014 | 2402AA
MULTIFUNCTIO
C063 | 849AA
MULTIFONCTIO
C005 | 1390AA
HEADLIGHT_HO
C034 | 3029AA
AUTO_HOLD_BR
C003 | 1216AA
ASSISTED_PAR
NOTE 17
VIEW A
NOTE 13
NOTE 14
BETWEEN NODES PF49 AND PF46, THE HARNESS MUST BE MANUFACTURED STRAIGHT ON JIG BOARD
IN ANY CASE OF ISSUE YAZAKI WILL NOT ACCEPT ANY CLAIM DUE TO CLIP TO BRANCH TAKE OUT POSITION IS NOT COMPLY TO GUIDELINE.
THE WEIGHTS FOR EACH PIE REFERENCE PRESENT IN THE TCC FOLIO _ ARE AVAILABLE IN NEWTON UNDER THE PIE REFERENCE PRESENT IN THE TITLE BLOCK
NOTE 1 : GENERAL REQUIREMENTS
1.1. PRODUCTION AND SUPPLY OF PRODUCTS ACCORDING TO THE STANDARD:00-10-515-U
1.2. PRODUCTION OF THE ELECTRICAL SUBSTRATES IN PARTS ACCORDING TO STANDARD:00-1903-2024-0002 V3.0
1.3. PART HAS TO BE COMPLIANT WITH 00-1903-2024-0001 V3.0 (WIRING REQUIREMENT AND TOLERANCE)
1.4. PART HAS TO BE COMPLIANT WITH 00-1903-2024-0003 V3.0 (FOR HIGH SPEED CONFIG)
NOTE 2 : MARKING
2.1. MARKING ACCORDING TO THE STANDARD:00-10-591-G
2.2. MARKING ACCORDING TO THE STANDARD:00-00-007-E
2.2.1. LOGOTYPE TYPE 1
2.2.2. PART NUMBER REFERENCE, 16 CHARACTERS
2.2.3. RENAULT PART INDEX, 3 CHARACTERS
2.2.4. DATE
2.2.5. YAZAKI SITE'S COMPANY NAME AND MANUFACTURING SITE
2.2.6. TEAM CODE
2.2.7. SUPPLIER'S QUALITY CONTROL CERTIFICATION
2.3. VISUALIZATION OF THE MARKING LABEL : SEE SHEET 1
2.4. LOCATION OF THE LABEL ON THE PART : SEE SHEET 1
NOTE 3 : HARNESS PATCH SPECIFICATION
3.1. SEALING STANDARD SPECIFIED : THE PATCH THAT HAS TO WILL BE SHIPPED CLOSED AND THE LEVERS OPEN, NOT GUARANTEED THE SEALING
3.2. THE PATCH MUST BE DESIGNED TO BE ASSEMBLED BY ENGINEERED LEVERS.
3.3. LOCATION OF INTERNAL HOOKS INSIDE PATCH AND COVERS ARE MANAGED BY THE SUPPLIER
3.4. PATCH MUST BE DESIGNED TO BE ASSEMBLED BY HAND
3.5. PATCH MUST NOT BE REUSED MORE THAN ONT OR HOOKED DURING ASSEMBLY.
3.6. THE PATCH MUST BE DESIGNED TO BE ASSEMBLED BY HAND WITHOUT TOOLS
3.7. THE MINIMUM SAFETY AND MODULATION OF THE SOLUTION OR OF THE NATURE AND ARRANGEMENT OF MECHANICAL PROTECTION (CHAIN TUBE) MUST BE APPROVED BY THE YAZAKI SAFETY RPI OF VEHICLE
GENERAL TOLERANCE ACCORDING TO ISO 8015
GENERAL TOLERANCE ACCORDING TO ISO 14405-1
- 1 DECIMAL TOLERANCE (BRANCH ONLY): 0mm / + 10mm
- 2 DECIMAL TOLERANCE (BRANCH ONLY): 0mm / + 5mm
GENERAL TOLERANCE ACCORDING TO ISO 14405-2
- 1 DECIMAL TOLERANCE (BRANCH ONLY): 0mm / + 10mm
- 2 DECIMAL TOLERANCE (BRANCH ONLY): 0mm / + 5mm
ANGULAR TOLERANCE ACCORDING TO ISO 14405-3
- 1 DECIMAL TOLERANCE = 0mm / + 90mm
- 2 DECIMAL TOLERANCE = 0mm / + 45mm
RADIUS TOLERANCE BETWEEN REFERENCES
MAXIMUM TOLERANCE ALLOWED BETWEEN POINTS
MAXIMUM TOLERANCE ALLOWED WHEN CROSSING
TOLERANCE OF SLOTTED HOLES ACCORDING TO ISO 2768-1
TOLERANCE OF SLOTTED COVER LENGTH:
- 1 DECIMAL = ± 0.5%
- 2 DECIMAL = ± 0.5% / ± 0.5%
- 3 DECIMAL = ± 0.5% / ± 0.5%
- 4 DECIMAL = ± 0.5%
3.8. ELECTRICAL COMPATIBILITY, ANY MODIFICATION OF THE TECHNICAL DEFINITION OF THE HARNESS THAT AFFECTS THE EMC REGULATORY PERFORMANCE BY ADDING OR REMOVING A POINTS OR SHIELDING MUST BE VALIDATED BY RENAULT ENGINEERING IN CONJUNCTION WITH THE TCR BEFORE 1ST IDENTIFICATION OF YEAR / FUTURE NUMBERS BY FIRMING COLOUR / ANY CHANGE OF THE TECHNICAL DEFINITION OF THE HARNESS THAT AFFECTS ITS MECHANICAL PERFORMANCE THE TECHNICAL SOLUTION MUST BE VALIDATED BY RENAULT ENGINEERING IN CONJUNCTION WITH THE TCR BEFORE 1ST IDENTIFICATION
2.2.5
2.2.1
2.2.2
2.2.3
2.2.4
2.2.6
2.2.7
CONFORMITY A LA NORME
LISTE VISIRAN1 ANNEXE 1
CONSISTENLY WITH STANDARD
VISIRAN1 LIST IN APPENDIX 1
01-00-510
-06
M : METALLIQUE/METALLIC
P : POLYMERE/POLYMER
M
P
PLAN SOUMIS A LA SIGNATURE
DRAWING SUBJECTED TO SIGNATURE
PLAN NON SOUMIS A LA SIGNATURE
DRAWING NOT SUBJECTED TO SIGNATURE
ISO GPS
SPECIFICATION DIMENSIONNELLE, GEOMETRIQUE ET D'ETATS DE SURFACE SELON LES TDS RTS 001 ET CONFORMENT A LA NORME RENAULT :
00-10-035 -B
DIMENSIONAL, GEOMETRICAL AND SURFACE TEXTURE SPECIFICATIONS ACCORDING TO TDS RTS 001 AND WITH ACCORDANCE TO THE RENAULT STANDARD :
00-10-035 -B
OPERATEUR DE SPECIFICATION DE TAILLE PAR DEFAUT
DEFAULT SPECIFICATION OPERATOR FOR SIZE :
TAILLE LINEAIRE ISO 14405 : ☐ SIZE/ISO
LINEAR SIZE ISO 14405 : ☐ 00.NO/NO
TOLERANCE ET TOLERANCEMENT DES PIECES NON RIGIDES
RLOW / DIMENSIONING AND TOLERANCING OF THE NON-RIGID PARTS IS CARRIED OUT IN ACCORDING TO :
ISO/DIN ☐ 00.NO/NO
11 ASSURE2 VOIR SUR LES CONDITIONS DE CONFORMITE A APPLIQUER SUR SPECIFIES : MAT SURE THAT THE CONDITIONS CONFORME TO BE APPLIED ARE SPECIFIED.
HIERARCHISATION DES CARACTERISTIQUES
NORME 01-13-321
CLASSIFICATION OF REQUIREMENTS
STANDARD 01-13-321
TOTALE
TOTAL
TOUTE CARACTERISTIQUE NON HIERARCHISEE EST DE NIVEAU 3
ANY CHARACTERISTIC NOT CLASSIFIED BELONGS TO LEVEL 3
WIRE - DEFNE
TCC - TCC_HCB_HCB_HCB40_TM01SE_-_H_EXCEL
FEDERATED 1
FDS
DFS57781G-1 / DFS577814-1 / DFS577898-1 / DFS577900-1 / DFS578658-1 / DFS578661-1 / DFS588333-1 / DFS588238-1 / DFS589077-1 / DFS589080-1 / DFS589082-1 / DFS589089-1 / DFS591419-1 / DFS591421-1 / DFS582007-1 / DFS583099-1 / DFS583101-1 / DFS583261-1 / DFS591101-1 / DFS591518-1 / DFS537291-1 / DFS537292-1 / DFS537293-1 / DFS537294-1 / DFS537295-1 / DFS537296-1 / DFS537297-1 / DFS537298-1 / DFS537299-1 / DFS537301-1 / DFS537302-1 / DFS537303-1 / DFS537304-1 / DFS537305-1 / DFS537306-1 / DFS537307-1 / DFS537308-1 / DFS537309-1 / DFS537310-1 / DFS537311-1 / DFS537312-1 / DFS537313-1 / DFS537314-1 / DFS537315-1 / DFS537316-1 / DFS537317-1 / DFS537318-1 / DFS537319-1 / DFS537320-1 / DFS537321-1 / DFS537322-1 / DFS537323-1 / DFS537324-1 / DFS537325-1 / DFS537326-1 / DFS537327-1 / DFS537328-1 / DFS537329-1 / DFS537330-1 / DFS537331-1 / DFS537332-1 / DFS537333-1 / DFS537334-1 / DFS537335-1 / DFS537336-1 / DFS537337-1 / DFS537338-1 / DFS537339-1 / DFS537340-1 / DFS537341-1 / DFS537342-1 / DFS537343-1 / DFS537344-1 / DFS537345-1 / DFS537346-1 / DFS537347-1 / DFS537348-1 / DFS537349-1 / DFS537350-1 / DFS537351-1 / DFS537352-1 / DFS537353-1 / DFS537354-1 / DFS537355-1 / DFS537356-1 / DFS537357-1 / DFS537358-1 / DFS537359-1 / DFS537360-1 / DFS537361-1 / DFS537362-1 / DFS537363-1 / DFS537364-1 / DFS537365-1 / DFS537366-1 / DFS537367-1 / DFS537368-1 / DFS537369-1 / DFS537370-1 / DFS537371-1 / DFS537372-1 / DFS537373-1 / DFS537374-1 / DFS537375-1 / DFS537376-1 / DFS537377-1 / DFS537378-1 / DFS537379-1 / DFS537380-1 / DFS537381-1 / DFS537382-1 / DFS537383-1 / DFS537384-1 / DFS537385-1 / DFS537386-1 / DFS537387-1 / DFS537388-1 / DFS537389-1 / DFS537390-1 / DFS537391-1 / DFS537392-1 / DFS537393-1 / DFS537394-1 / DFS537395-1 / DFS537396-1 / DFS537397-1 / DFS537398-1 / DFS537399-1 / DFS537400-1 / DFS537401-1 / DFS537402-1 / DFS537403-1 / DFS537404-1 / DFS537405-1 / DFS537406-1 / DFS537407-1 / DFS537408-1 / DFS537409-1 / DFS537410-1 / DFS537411-1 / DFS537412-1 / DFS537413-1 / DFS537414-1 / DFS537415-1 / DFS537416-1 / DFS537417-1 / DFS537418-1 / DFS537419-1 / DFS537420-1 / DFS537421-1 / DFS537422-1 / DFS537423-1 / DFS537424-1 / DFS537425-1 / DFS537426-1 / DFS537427-1 / DFS537428-1 / DFS537429-1 / DFS537430-1 / DFS537431-1 / DFS537432-1 / DFS537433-1 / DFS537434-1 / DFS537435-1 / DFS537436-1 / DFS537437-1 / DFS537438-1 / DFS537439-1 / DFS537440-1 / DFS537441-1 / DFS537442-1 / DFS537443-1 / DFS537444-1 / DFS537445-1 / DFS537446-1 / DFS537447-1 / DFS537448-1 / DFS537449-1 / DFS537450-1 / DFS537451-1 / DFS537452-1 / DFS537453-1 / DFS537454-1 / DFS537455-1 / DFS537456-1 / DFS537457-1 / DFS537458-1 / DFS537459-1 / DFS537460-1 / DFS537461-1 / DFS537462-1 / DFS537463-1 / DFS537464-1 / DFS537465-1 / DFS537466-1 / DFS537467-1 / DFS537468-1 / DFS537469-1 / DFS537470-1 / DFS537471-1 / DFS537472-1 / DFS537473-1 / DFS537474-1 / DFS537475-1 / DFS537476-1 / DFS537477-1 / DFS537478-1 / DFS537479-1 / DFS537480-1 / DFS537481-1 / DFS537482-1 / DFS537483-1 / DFS537484-1 / DFS537485-1 / DFS537486-1 / DFS537487-1 / DFS537488-1 / DFS537489-1 / DFS537490-1 / DFS537491-1 / DFS537492-1 / DFS537493-1 / DFS537494-1 / DFS537495-1 / DFS537496-1 / DFS537497-1 / DFS537498-1 / DFS537499-1 / DFS537500-1 / DFS537501-1 / DFS537502-1 / DFS537503-1 / DFS537504-1 / DFS537505-1 / DFS537506-1 / DFS537507-1 / DFS537508-1 / DFS537509-1 / DFS537510-1 / DFS537511-1 / DFS537512-1 / DFS537513-1 / DFS537514-1 / DFS537515-1 / DFS537516-1 / DFS537517-1 / DFS537518-1 / DFS537519-1 / DFS537520-1 / DFS537521-1 / DFS537522-1 / DFS537523-1 / DFS537524-1 / DFS537525-1 / DFS537526-1 / DFS537527-1 / DFS537528-1 / DFS537529-1 / DFS537530-1 / DFS537531-1 / DFS537532-1 / DFS537533-1 / DFS537534-1 / DFS537535-1 / DFS537536-1 / DFS537537-1 / DFS537538-1 / DFS537539-1 / DFS537540-1 / DFS537541-1 / DFS537542-1 / DFS537543-1 / DFS537544-1 / DFS537545-1 / DFS537546-1 / DFS537547-1 / DFS537548-1 / DFS537549-1 / DFS537550-1 / DFS537551-1 / DFS537552-1 / DFS537553-1 / DFS537554-1 / DFS537555-1 / DFS537556-1 / DFS537557-1 / DFS537558-1 / DFS537559-1 / DFS537560-1 / DFS537561-1 / DFS537562-1 / DFS537563-1 / DFS537564-1 / DFS537565-1 / DFS537566-1 / DFS537567-1 / DFS537568-1 / DFS537569-1 / DFS537570-1 / DFS537571-1 / DFS537572-1 / DFS537573-1 / DFS537574-1 / DFS537575-1 / DFS537576-1 / DFS537577-1 / DFS537578-1 / DFS537579-1 / DFS537580-1 / DFS537581-1 / DFS537582-1 / DFS537583-1 / DFS537584-1 / DFS537585-1 / DFS537586-1 / DFS537587-1 / DFS537588-1 / DFS537589-1 / DFS537590-1 / DFS537591-1 / DFS537592-1 / DFS537593-1 / DFS537594-1 / DFS537595-1 / DFS537596-1 / DFS537597-1 / DFS537598-1 / DFS537599-1 / DFS537600-1 / DFS537601-1 / DFS537602-1 / DFS537603-1 / DFS537604-1 / DFS537605-1 / DFS537606-1 / DFS537607-1 / DFS537608-1 / DFS537609-1 / DFS537610-1 / DFS537611-1 / DFS537612-1 / DFS537613-1 / DFS537614-1 / DFS537615-1 / DFS537616-1 / DFS537617-1 / DFS537618-1 / DFS537619-1 / DFS537620-1 / DFS537621-1 / DFS537622-1 / DFS537623-1 / DFS537624-1 / DFS537625-1 / DFS537626-1 / DFS537627-1 / DFS537628-1 / DFS537629-1 / DFS537630-1 / DFS537631-1 / DFS537632-1 / DFS537633-1 / DFS537634-1 / DFS537635-1 / DFS537636-1 / DFS537637-1 / DFS537638-1 / DFS537639-1 / DFS537640-1 / DFS537641-1 / DFS537642-1 / DFS537643-1 / DFS537644-1 / DFS537645-1 / DFS537646-1 / DFS537647-1 / DFS537648-1 / DFS537649-1 / DFS537650-1 / DFS537651-1 / DFS537652-1 / DFS537653-1 / DFS537654-1 / DFS537655-1 / DFS537656-1 / DFS537657-1 / DFS537658-1 / DFS537659-1 / DFS537660-1 / DFS537661-1 / DFS537662-1 / DFS537663-1 / DFS537664-1 / DFS537665-1 / DFS537666-1 / DFS537667-1 / DFS537668-1 / DFS537669-1 / DFS537670-1 / DFS537671-1 / DFS537672-1 / DFS537673-1 / DFS537674-1 / DFS537675-1 / DFS537676-1 / DFS537677-1 / DFS537678-1 / DFS537679-1 / DFS537680-1 / DFS537681-1 / DFS537682-1 / DFS537683-1 / DFS537684-1 / DFS537685-1 / DFS537686-1 / DFS537687-1 / DFS537688-1 / DFS537689-1 / DFS537690-1 / DFS537691-1 / DFS537692-1 / DFS537693-1 / DFS537694-1 / DFS537695-1 / DFS537696-1 / DFS537697-1 / DFS537698-1 / DFS537699-1 / DFS537700-1 / DFS537701-1 / DFS537702-1 / DFS537703-1 / DFS537704-1 / DFS537705-1 / DFS537706-1 / DFS537707-1 / DFS537708-1 / DFS537709-1 / DFS537710-1 / DFS537711-1 / DFS537712-1 / DFS537713-1 / DFS537714-1 / DFS537715-1 / DFS537716-1 / DFS537717-1 / DFS537718-1 / DFS537719-1 / DFS537720-1 / DFS537721-1 / DFS537722-1 / DFS537723-1 / DFS537724-1 / DFS537725-1 / DFS537726-1 / DFS537727-1 / DFS537728-1 / DFS537729-1 / DFS537730-1 / DFS537731-1 / DFS537732-1 / DFS537733-1 / DFS537734-1 / DFS537735-1 / DFS537736-1 / DFS537737-1 / DFS537738-1 / DFS537739-1 / DFS537740-1 / DFS537741-1 / DFS537742-1 / DFS537743-1 / DFS537744-1 / DFS537745-1 / DFS537746-1 / DFS537747-1 / DFS537748-1 / DFS537749-1 / DFS537750-1 / DFS537751-1 / DFS537752-1 / DFS537753-1 / DFS537754-1 / DFS537755-1 / DFS537756-1 / DFS537757-1 / DFS537758-1 / DFS537759-1 / DFS537760-1 / DFS537761-1 / DFS537762-1 / DFS537763-1 / DFS537764-1 / DFS537765-1 / DFS537766-1 / DFS537767-1 / DFS537768-1 / DFS537769-1 / DFS537770-1 / DFS537771-1 / DFS537772-1 / DFS537773-1 / DFS537774-1 / DFS537775-1 / DFS537776-1 / DFS537777-1 / DFS537778-1 / DFS537779-1 / DFS537780-1 / DFS537781-1 / DFS537782-1 / DFS537783-1 / DFS537784-1 / DFS537785-1 / DFS537786-1 / DFS537787-1 / DFS537788-1 / DFS537789-1 / DFS537790-1 / DFS537791-1 / DFS537792-1 / DFS537793-1 / DFS537794-1 / DFS537795-1 / DFS537796-1 / DFS537797-1 / DFS537798-1 / DFS537799-1 / DFS537800-1 / DFS537801-1 / DFS537802-1 / DFS537803-1 / DFS537804-1 / DFS537805-1 / DFS537806-1 / DFS537807-1 / DFS537808-1 / DFS537809-1 / DFS537810-1 / DFS537811-1 / DFS537812-1 / DFS537813-1 / DFS537814-1 / DFS537815-1 / DFS537816-1 / DFS537817-1 / DFS537818-1 / DFS537819-1 / DFS537820-1 / DFS537821-1 / DFS537822-1 / DFS537823-1 / DFS537824-1 / DFS537825-1 / DFS537826-1 / DFS537827-1 / DFS537828-1 / DFS537829-1 / DFS537830-1 / DFS537831-1 / DFS537832-1 / DFS537833-1 / DFS537834-1 / DFS537835-1 / DFS537836-1 / DFS537837-1 / DFS537838-1 / DFS537839-1 / DFS537840-1 / DFS537841-1 / DFS537842-1 / DFS537843-1 / DFS537844-1 / DFS537845-1 / DFS537846-1 / DFS537847-1 / DFS537848-1 / DFS537849-1 / DFS537850-1 / DFS537851-1 / DFS537852-1 / DFS537853-1 / DFS537854-1 / DFS537855-1 / DFS537856-1 / DFS537857-1 / DFS537858-1 / DFS537859-1 / DFS537860-1 / DFS537861-1 / DFS537862-1 / DFS537863-1 / DFS537864-1
APPLIED AFTER THE FI : DFS602361-1 / DFS602364-1
YAZAKI
YAZAKI SYSTEMES TECHNOLOGIQUES FRANCE SAS
2 RUE RENE CALDAIRON,BATIMENT B
78700 CONFLANS-SAINTE-HONORINE FRANCE
CABLAGE PLANCHE BORD DD
RHD DASHBOARD
DRAWN BY
E.UCAR
DATE
06020306
DRAWING REALISED WITH: IAE SIEMENS
CHECKED BY
M.GIRSIN
PROJECT
HCB
D.PART NUMBER
DCCP080VFK
SI REV
021
HARNESS STATUS
Released
MADE
DEFNE
PG NUMBER
200078951P
PG REV
-G
THIS DRAWING IS THE EXCLUSIVE PROPERTY OF YAZAKI SYSTEMES TECHNOLOGIES FRANCE SAS AND CANNOT BE COPIED OR DISCLOSED TO ANY PROGRAM NEEDS ON STRICTLY CONFIDENTIAL BASE
FORMAT
2xA0
HARNESS WEIGHT
SHEET
1/14